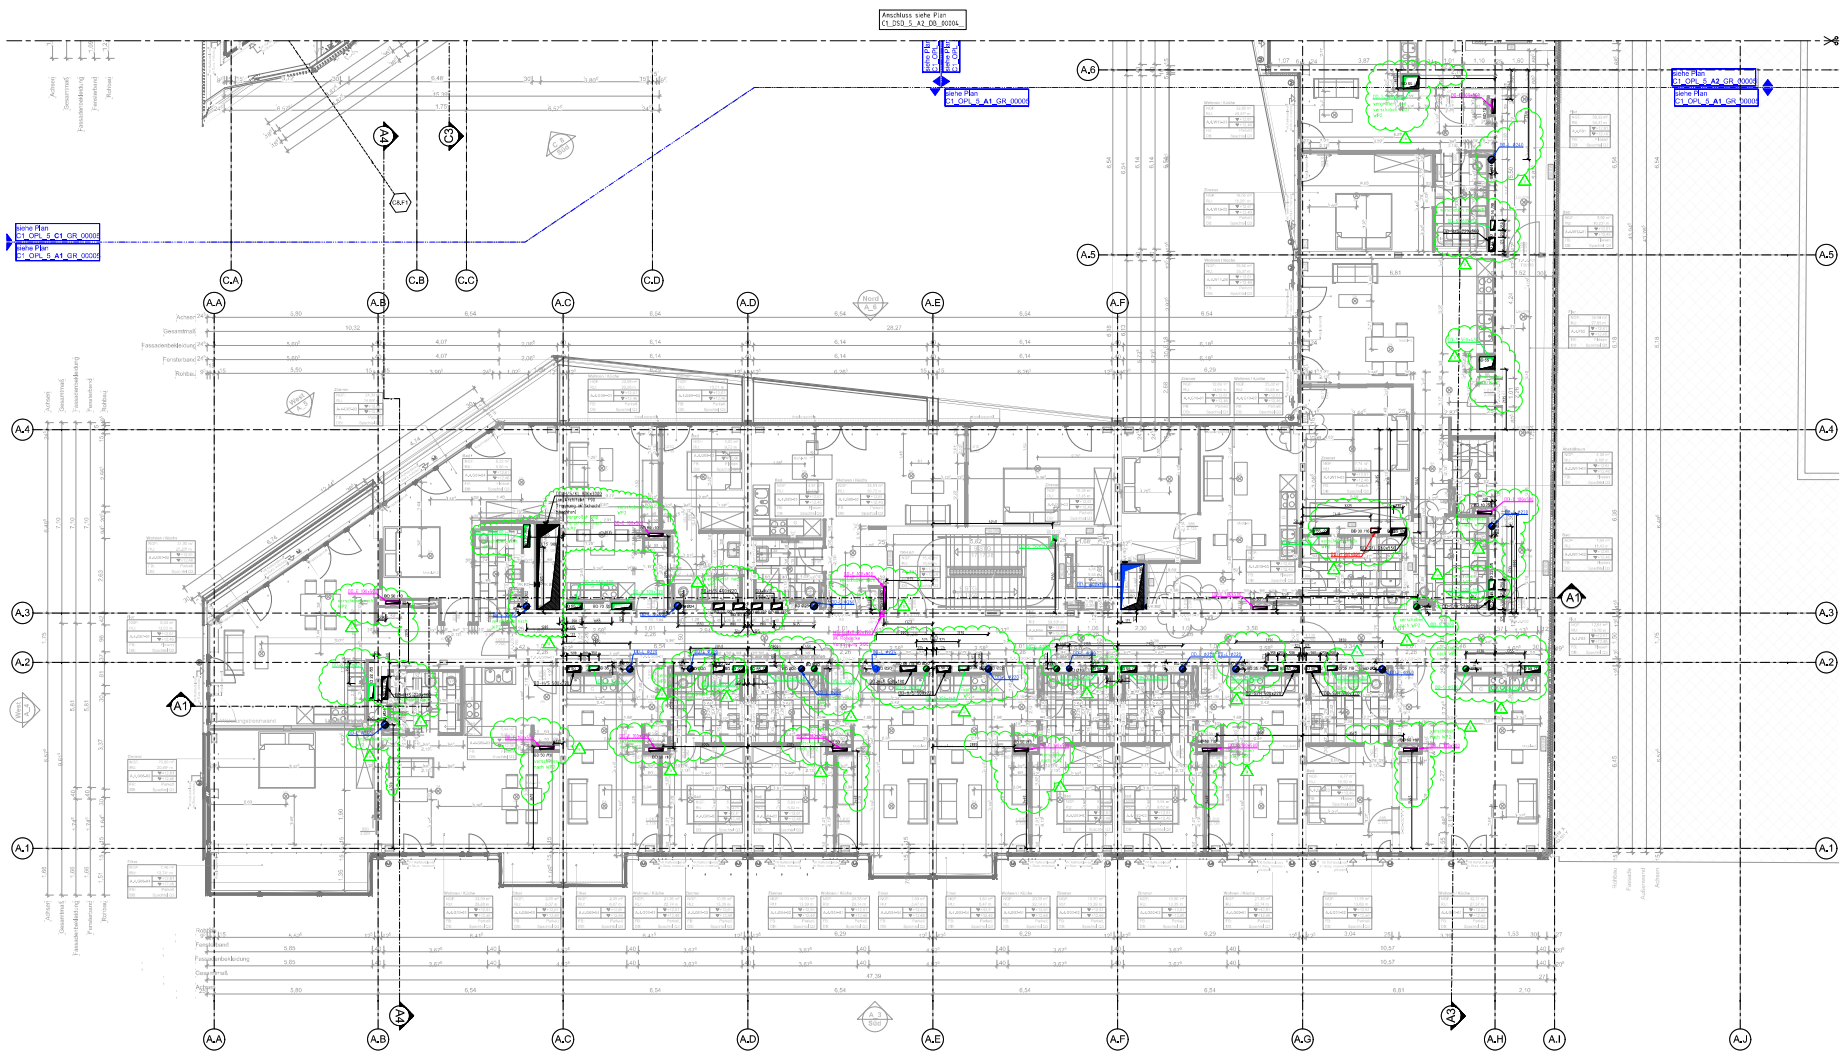

LEGENDE

Sanitaer

- M4.A Wanddurchbruch
- M4.C Deckendurchbruch
- M4.D Bodendurchbruch
- M5.F Wandschlitz
- M5.G Bodenschlitz
- M6.A Wanddurchbruch, rund
- M6.B Deckendurchbruch
- M6.C Bodendurchbruch

Elektro

- M4.A Wanddurchbruch
- M4.C Deckendurchbruch
- M4.D Bodendurchbruch
- M5.F Wandschlitz
- M5.G Bodenschlitz
- M6.A Wanddurchbruch, rund
- M6.B Deckendurchbruch
- M6.C Bodendurchbruch

Lueftung

- M4.A Wanddurchbruch
- M4.C Deckendurchbruch
- M4.D Bodendurchbruch
- M5.F Wandschlitz
- M5.G Bodenschlitz
- M6.A Wanddurchbruch, rund
- M6.B Deckendurchbruch
- M6.C Bodendurchbruch

Heizung/Kaelte

- M4.A.W Wanddurchbruch
- M4.B.W Deckendurchbruch
- M4.C.W Bodendurchbruch
- M5.F.W Wandschlitz
- M5.G.W Bodenschlitz
- M6.A.W Wanddurchbruch, rund
- M6.B.W Deckendurchbruch
- M6.C.W Bodendurchbruch

M5.F.4.250 (BA:+250 UKRD)
M5.F.5.500x200 (BA:+400 UKRD)
M5.F.6.1000x200

Hinweis Projektbeteiligte
Vermaßung nur von Achsen!

Planstatus	Phase	Bau-Nr.	LPH	Bereich	Ebene	Bau-Teil	Plan-Nr.
							A1.DB00004

C1_DSD_5_A1_DB_00004_a- -

Schlitz- und Durchbruchsangaben, Haus A, 4.OG Teil 1/2

Generalplaner: GRAFT
Gesellschaft von Architekten mbH
Friedrichstraße 50, 10252 Berlin, Germany
T +49 (30) 20 60 16 20
F +49 (30) 20 60 16 22
www.graft.de | info@graft.de

PLAN

Bauherr: PSD Projekt Zimmerstraße GmbH
Hochtief Bid Management GmbH
Zimmerstraße 56
10117 Berlin
tel. 030 20370100
fax 030 20370119
info@psd-berlin.com

Fachplaner: BERATEN | PLANEN | ÜBERWACHEN
Geiler Deutsche Energie-Consult GmbH
Auguststraße 32, 10119 Berlin
Telefon: (030) 81 00 81 - 30
Fax: (030) 81 00 81 - 33
hello@deutsche-energie.de
www.deutsche-energie.de

Verteiler und Verteilerergänzung:

Projekt: Charlie 01
Zimmerstraße GmbH, 10117 Berlin

0	A1	Rohfassungen ohne Aussparungen
1	A1	Rohfassungen mit Aussparungen
2	A1	Ausführungen
3	A1	Revisionsunterlage

Höhe ± 0,00 entspricht 35,30 m ÜNHN

zu erwartender höchster Grundwasserstand (zaHGW) = -5,00 m entspricht 30,10 m ÜNHN

Planausschnitt

N

Nutzungsartenplan: Ausführungsplanung

Format	Maßstab	Gezeichnet	Nachgeprüft	Abgeschlossen
594x841	1:50	Jerzinck	20.01.2017	01.06.2017

Dateiname: C1_OPL_5_A1_GR_00004_V3_- 10.03.2017